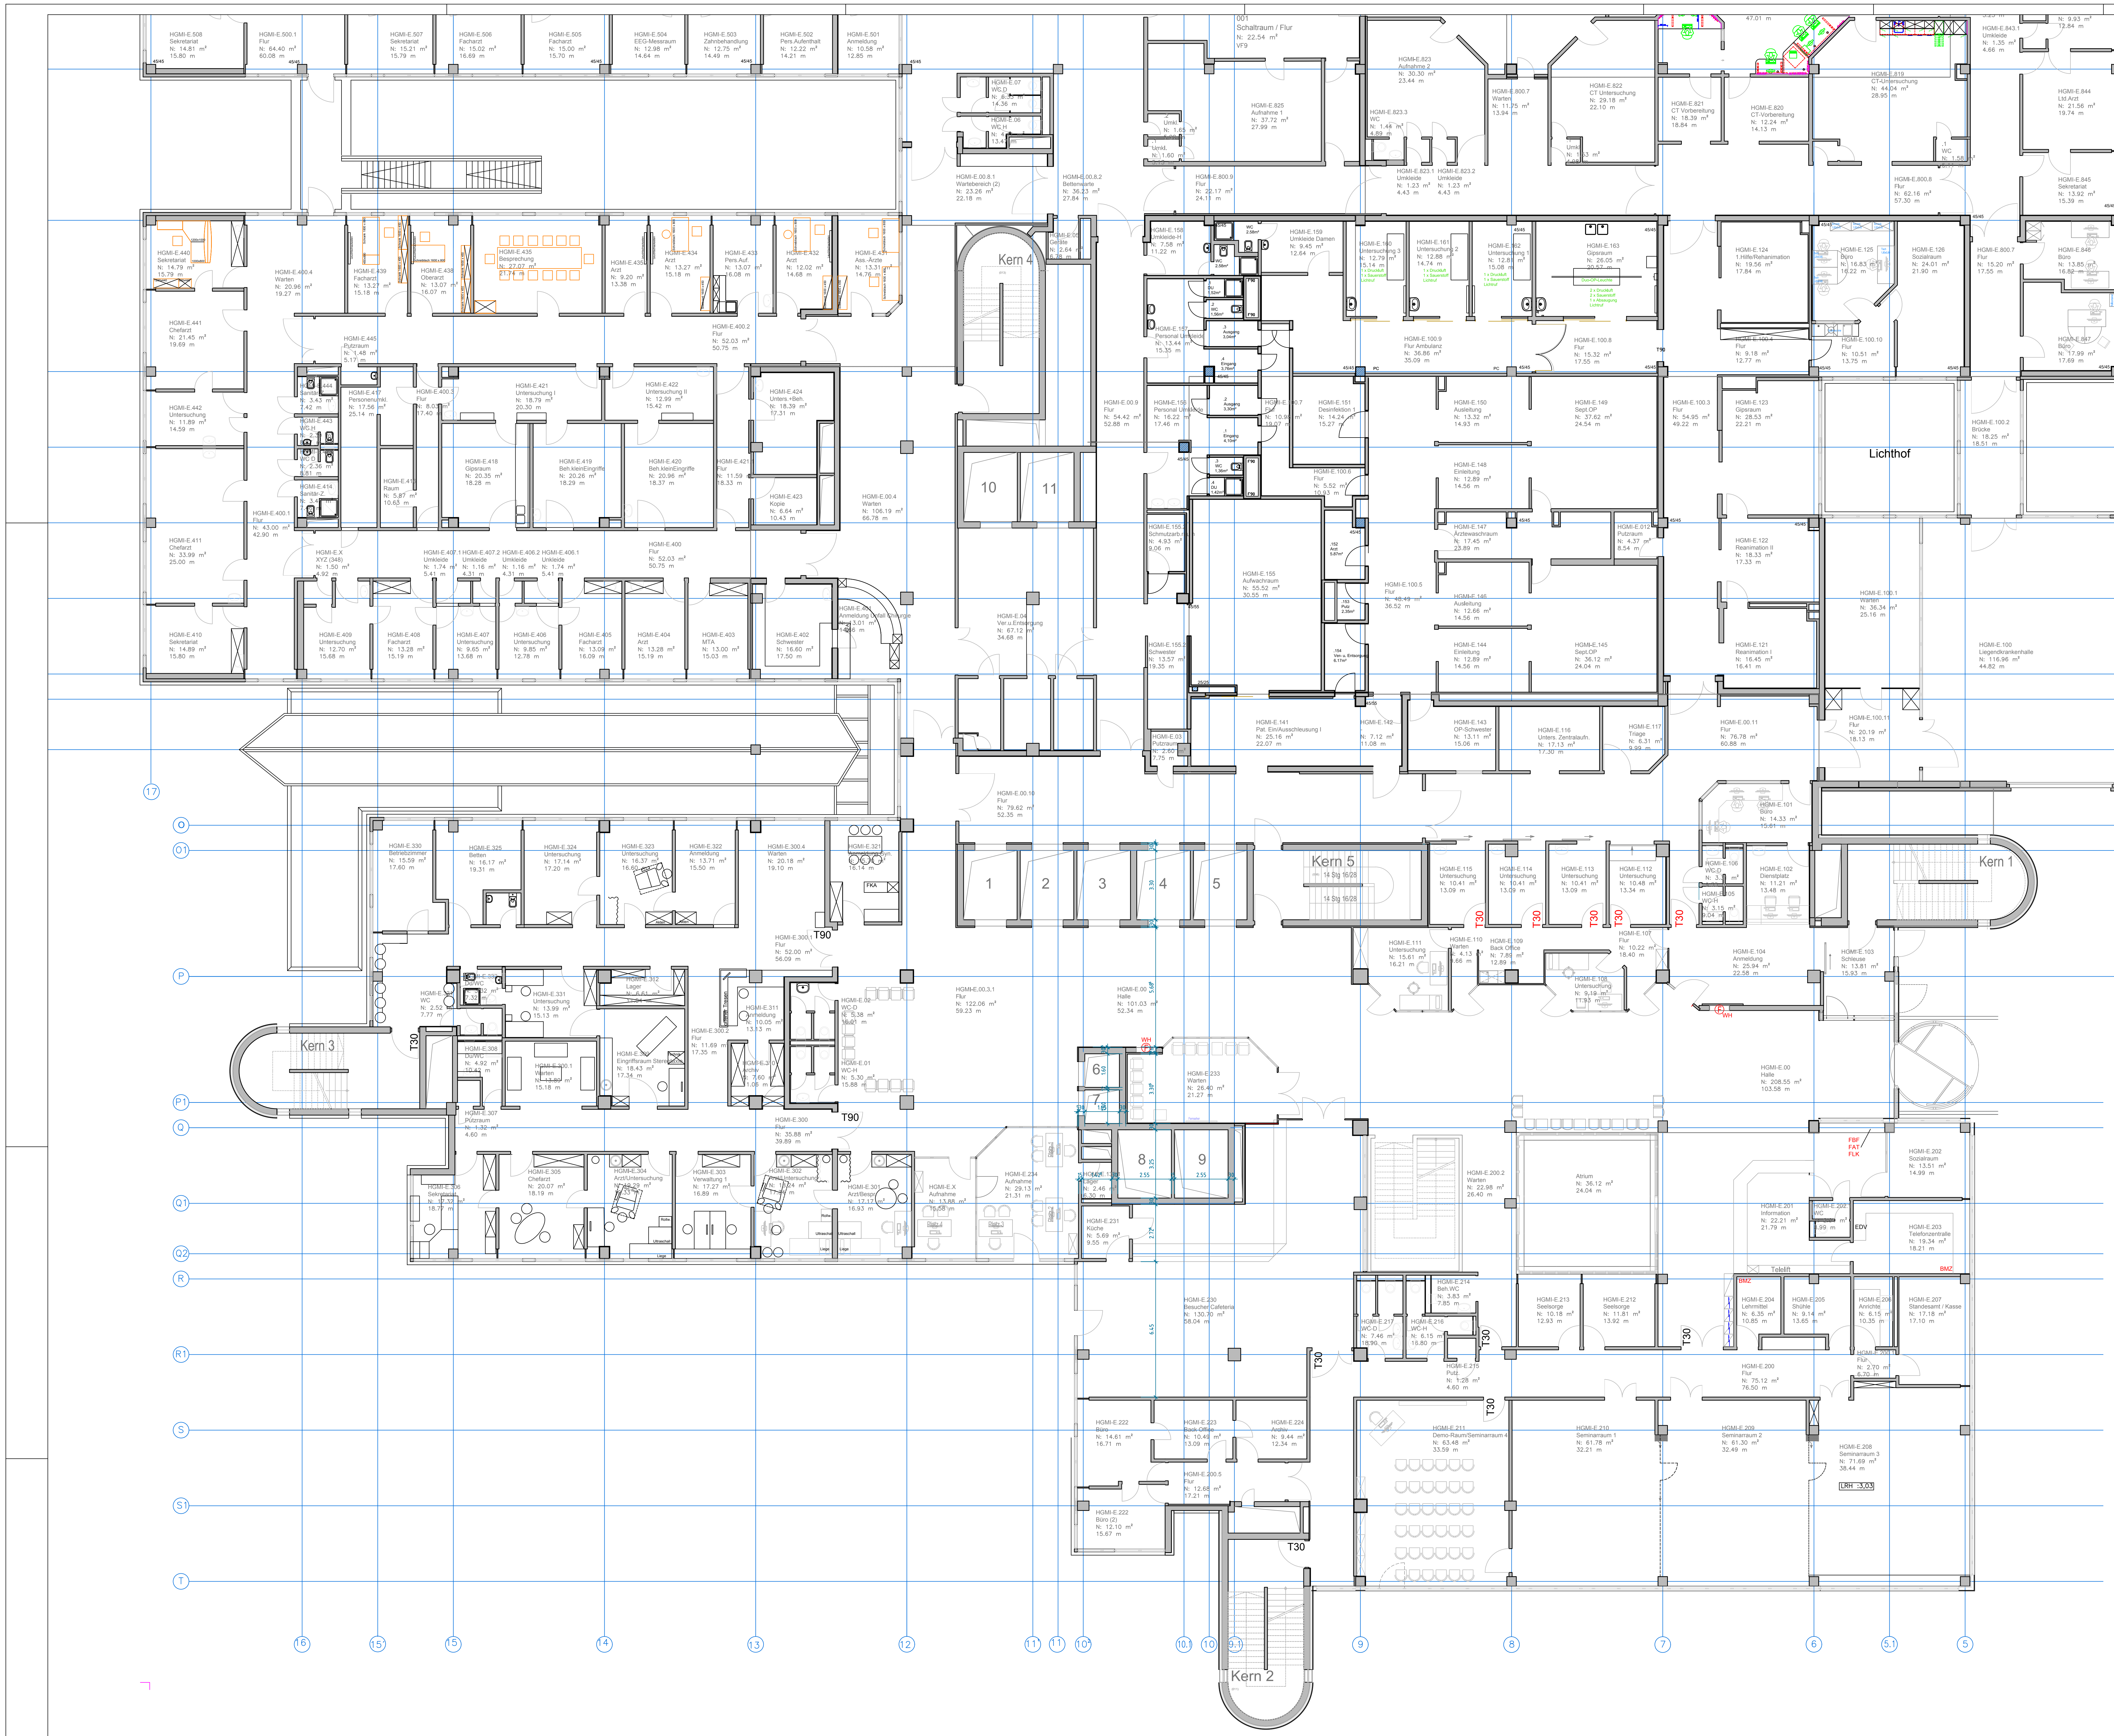

LEGENDE / BRANDSCHUTZ

🟪 Brandwand	
🟦 F90	
🟨 F30	

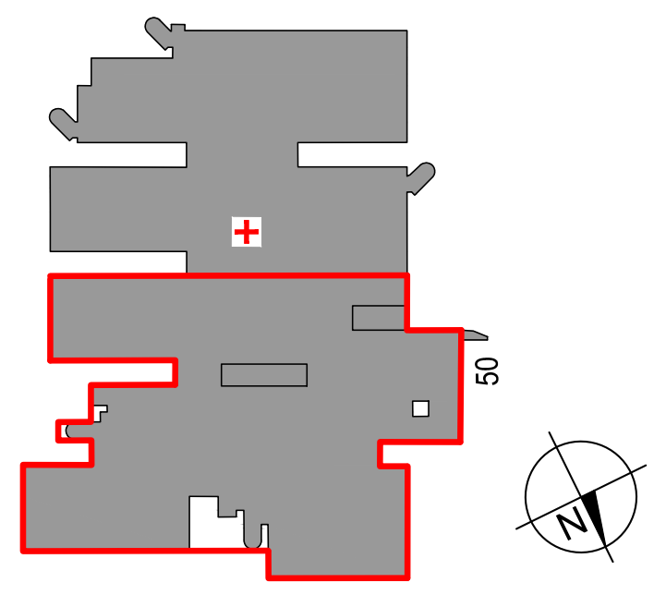

Index	Datum	Änderung	Name

Projekt:

Bauherr: Klinikum Bielefeld gem. GmbH
Teutoburger Strasse 50
33604 Bielefeld

klinikumbielefeld
unsere kompetenz für ihre gesundheit

Standort: Klinikum Bielefeld
Teutoburger Strasse 50
33604 Bielefeld

Planbezeichnung:

Grundriss Erdgeschoss Bestand / Teil 1

Gebäude: HGMI		Bauteil: .	Ebene: E
Gewerk: ART	Leistungsphase: Bestand	Datum Index: .	Index: .
Erstellt am: 10.08.2023	Erstellt von: K.Kaufhold/I.Schulz	Blattgröße: A0	Massstab: 1:100
Geprüft am:	Geprüft von:	Vermerk:	
Projektnummer: .	Zeichnungsnummer: .		

Dateiname: ARTB-HGMI-E.dwg

Referenz: